


חוברת נגרות
שם לקוח: משרד TEOMIM
משרד – פארק המדע נס ציונה
15.12.25

TEOMIM! INTERIOR DESIGN STUDIO Aleksey Molochnik Interior Designer 054-5553187 aleksey@teomim.co.il Sergey Molochnik Interior Designer 054-5553186 sergey@teomim.co.il Lazarov 33 St, Rishon LeZion <td>פרויקט: משרד נס ציונה TEOMIM</td> <td>הערות: * מידות סופיות לביצוע – לאחר מדידה בשטח בלבד. * תאום מול היועצים באחריות הקבלן המבצע. * במקרה של שינוי בשטח או אי התאמה יש להודיע למעצבת פנים מראש ולא לבצע כלא אישורה. * כל הפיגות בגרונג אלא אם מצוין בתוכניות אחרת. * פרזולים ויישומם בנגרות יתואמו מול המעצבת פנים. * יש לתאם עם מנהל הפרויקט ולקבל אישור מעצבת הפנים לגבי הכנות עבור: ציוד חשמל, תאורה, אודיו וידאו, מיזוג אויר וכיו"ב. * על הנגר להכין SHOP DRAWINGS לאחר מדידה בשטח (ולציין בהן נקודות חשמל ותקשורת) לעיון ואישור המעצבת פנים.</td> <td> לעיון למכרז לביצוע ☐☒☐ </td> <td>Floor: קומה: Room: חדר: Carpenty No.: מט' נגרות: Scale: קנ"מ: Date: תאריך: Page: גיליון:</td> <td> 1:25 15.12.25 01 </td>	פרויקט: משרד נס ציונה TEOMIM	הערות: * מידות סופיות לביצוע – לאחר מדידה בשטח בלבד. * תאום מול היועצים באחריות הקבלן המבצע. * במקרה של שינוי בשטח או אי התאמה יש להודיע למעצבת פנים מראש ולא לבצע כלא אישורה. * כל הפיגות בגרונג אלא אם מצוין בתוכניות אחרת. * פרזולים ויישומם בנגרות יתואמו מול המעצבת פנים. * יש לתאם עם מנהל הפרויקט ולקבל אישור מעצבת הפנים לגבי הכנות עבור: ציוד חשמל, תאורה, אודיו וידאו, מיזוג אויר וכיו"ב. * על הנגר להכין SHOP DRAWINGS לאחר מדידה בשטח (ולציין בהן נקודות חשמל ותקשורת) לעיון ואישור המעצבת פנים.	לעיון למכרז לביצוע ☐☒☐	Floor: קומה: Room: חדר: Carpenty No.: מט' נגרות: Scale: קנ"מ: Date: תאריך: Page: גיליון:	1:25 15.12.25 01
--	---------------------------------	---	---	---	---

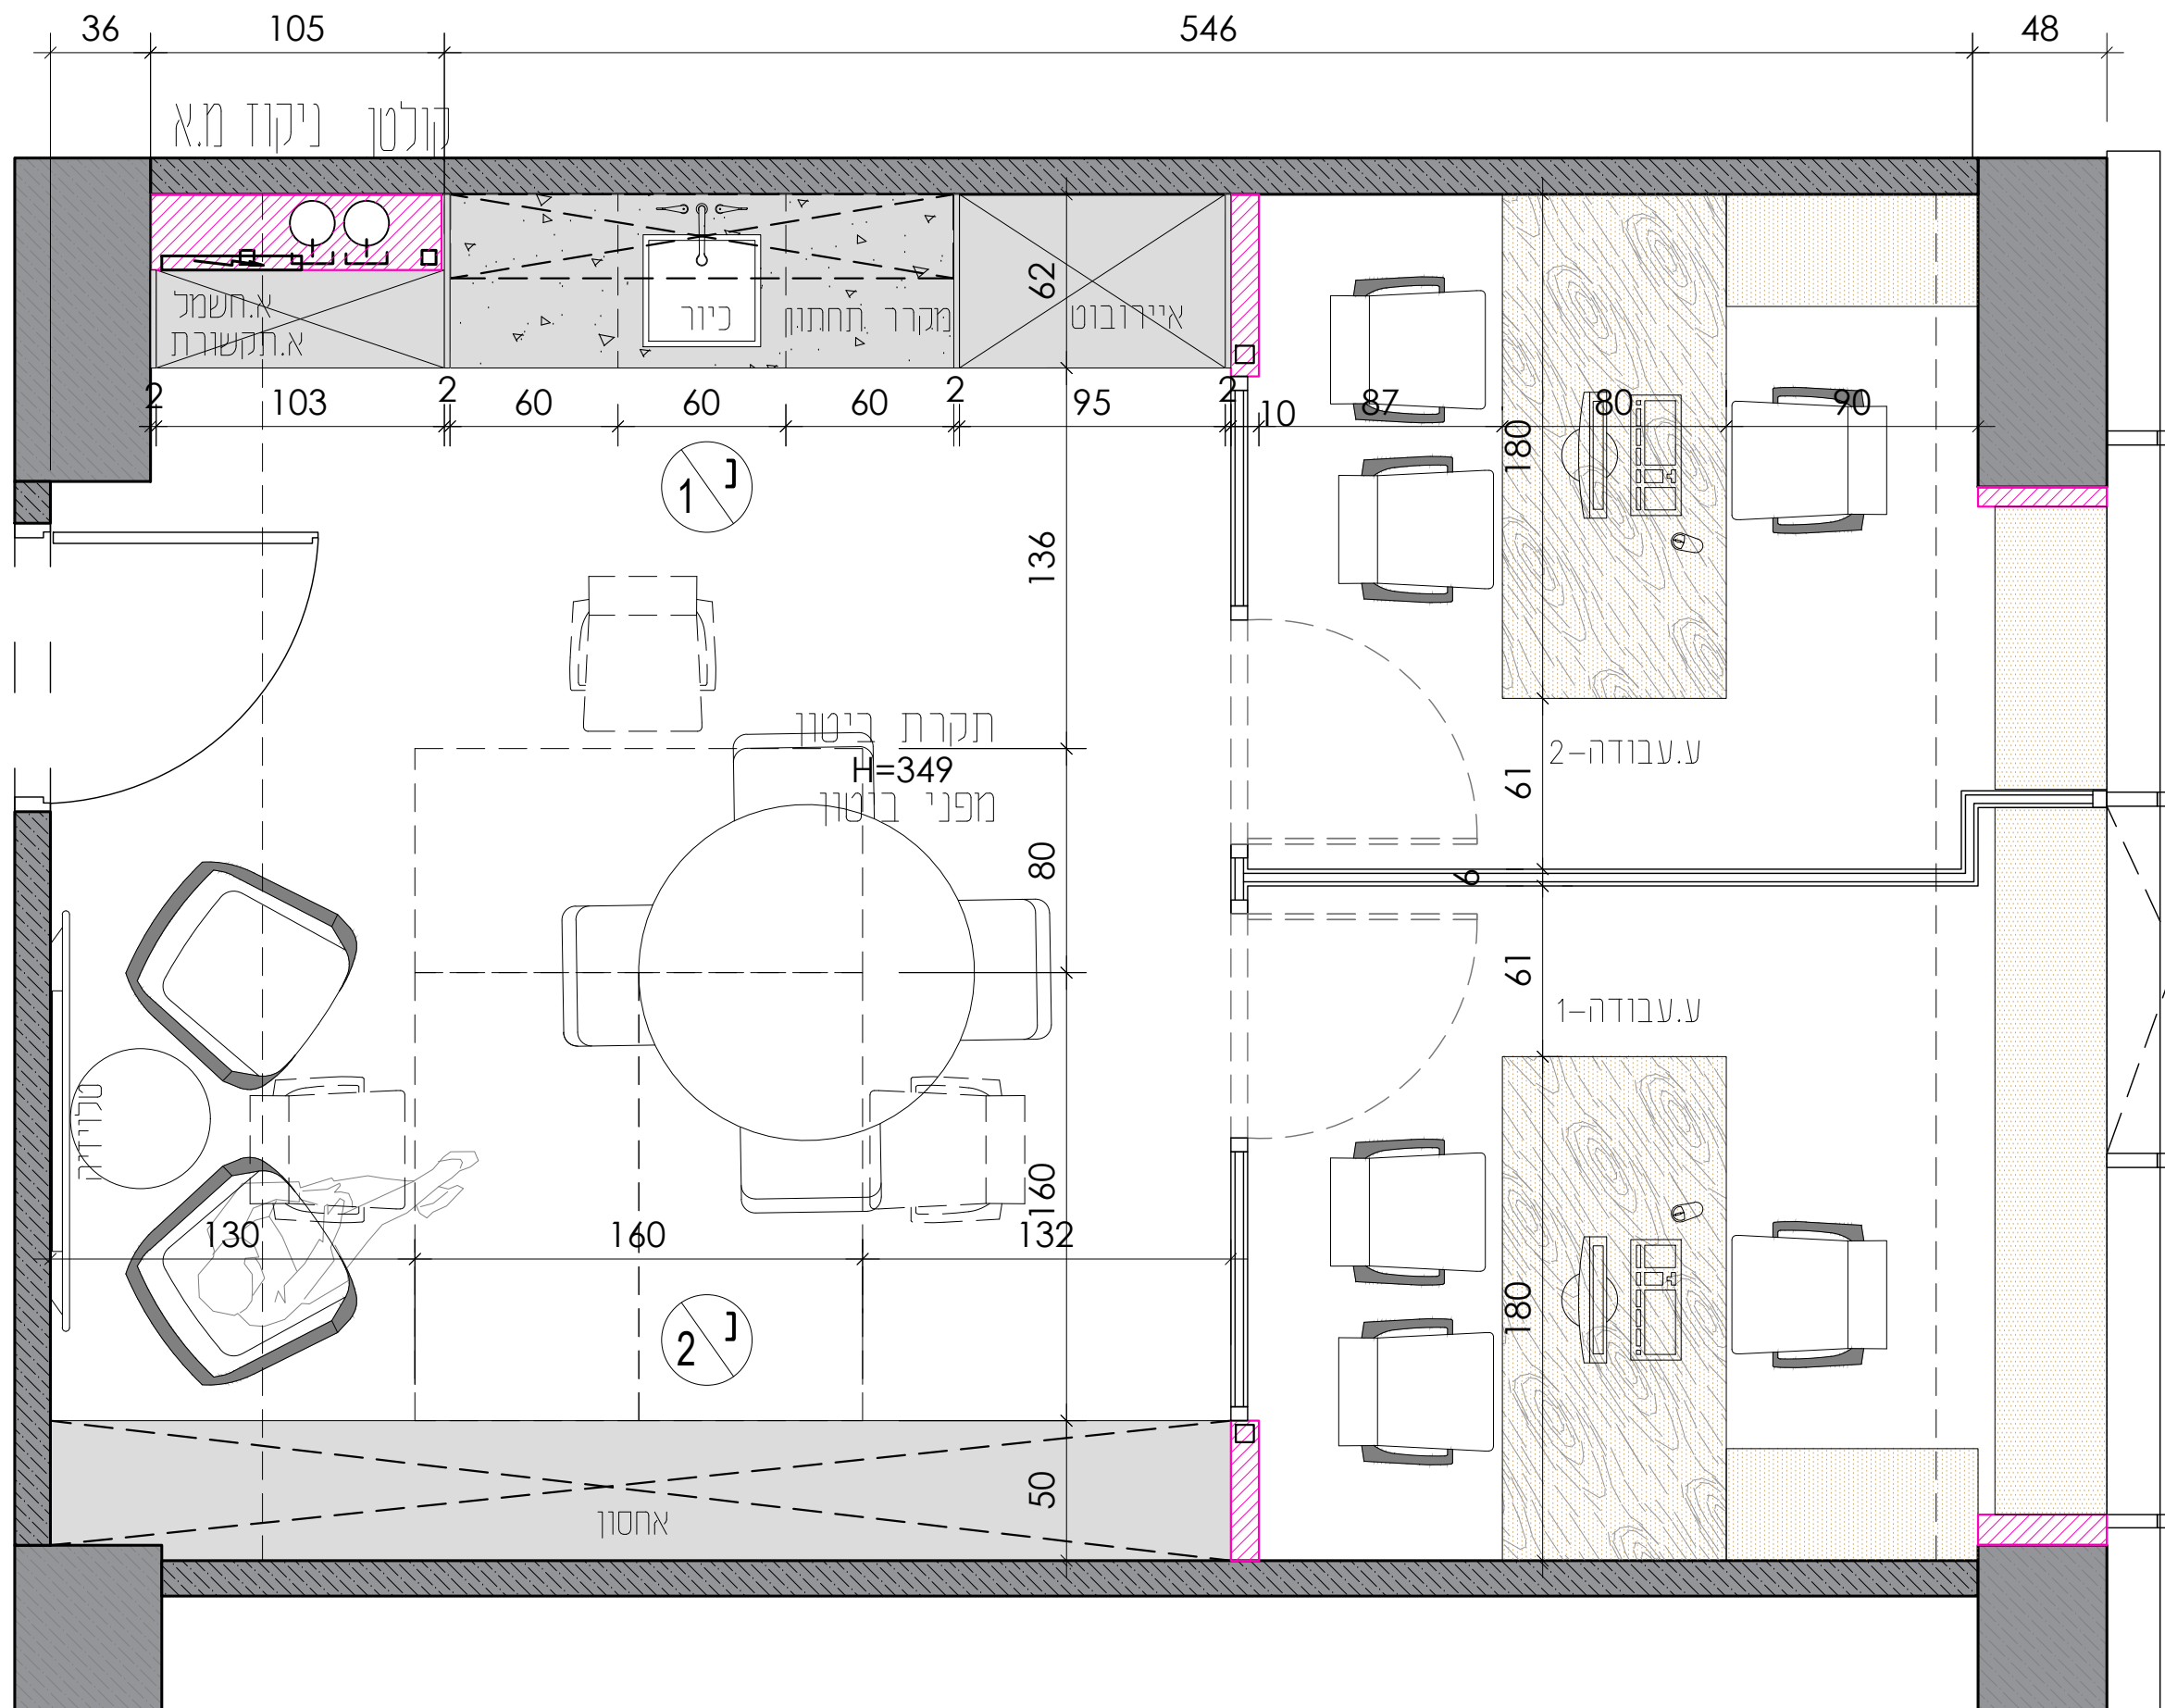

TEOMIM!

INTERIOR DESIGN STUDIO

Aleksey Molochnik
Interior Designer
054-5553187
aleksey@teomim.co.il

Sergey Molochnik
Interior Designer
054-5553186
sergey@teomim.co.il

Lazarov 33 St, Rishon LeZion

Project: פרויקט:

משרד נס ציונה

TEOMIM

הערות:
* מידות סופיות לביצוע - לאחר מדידה בשטח בלבד.
* תאום מול היועצים באחריות הקבלן המבצע.
* במקרה של שינוי בשטח או אי התאמה יש להודיע למעצבת פנים מראש ולא לבצע כלא אישורה.
* כל הפינות בגרונג אלא אם מצוין בתוכנית אחרת.
* פרזולים ויישומם בנגרות יתואמו מול המעצבת פנים.
* יש לתאם עם מנהל הפרויקט ולקבל אישור מעצבת הפנים לגבי הכנות עבור: ציוד חשמל, תאורה, אודיו וידאו, מיזוג אוויר וכיו"ב.
* על הגר להכין SHOP DRAWINGS לאחר מדידה בשטח (ולציין בהן נקודות חשמל ותקשורת) לעיון ואישור המעצבת פנים.

לעיון ☐
למכרז ☒
לביצוע ☐

Floor:

קומה:

Room:

חדר:

Carpentry No.:

מס' נגרות:

Scale: קנ"מ:

Date:

תאריך:



Page: גיליון:

ת.העמדה


1:25

15.12.25


02

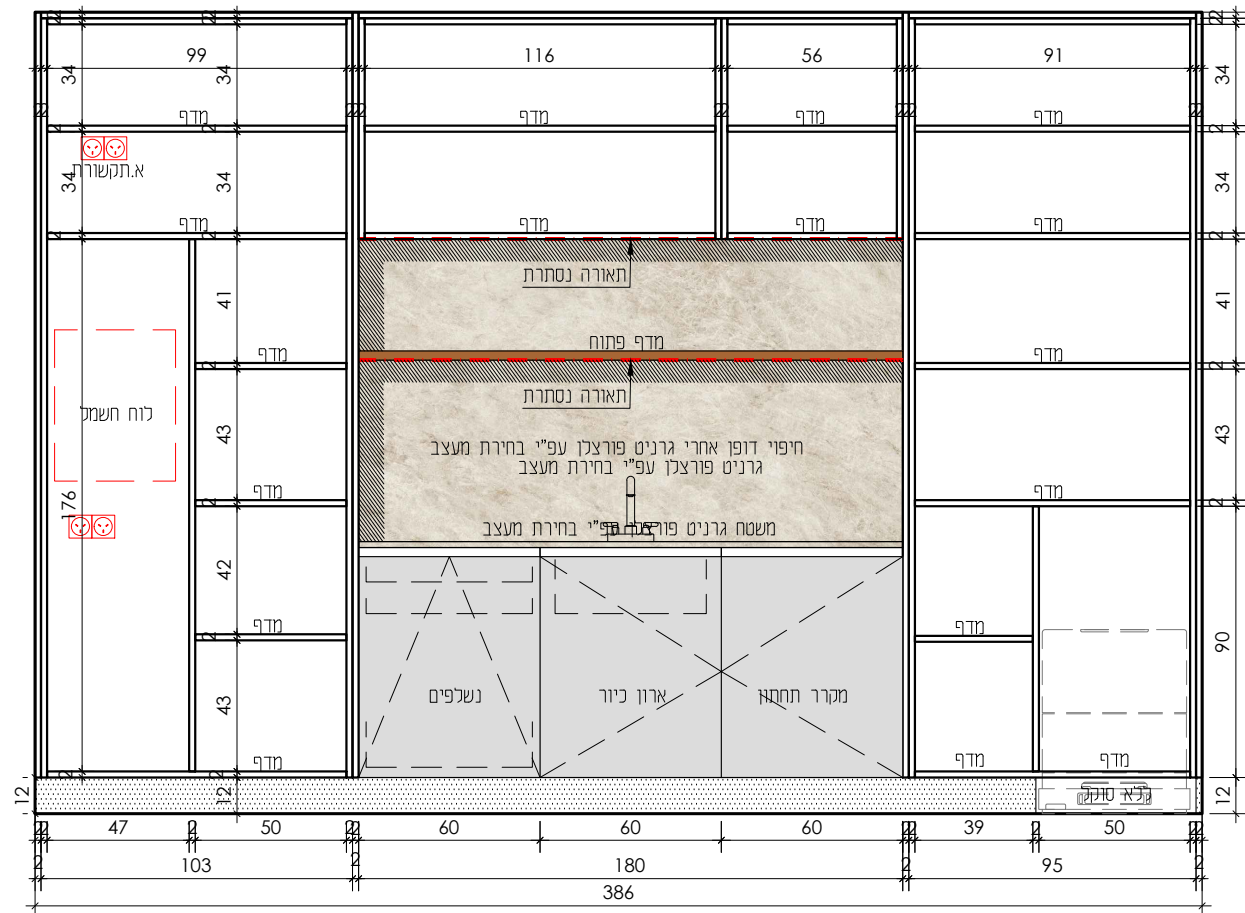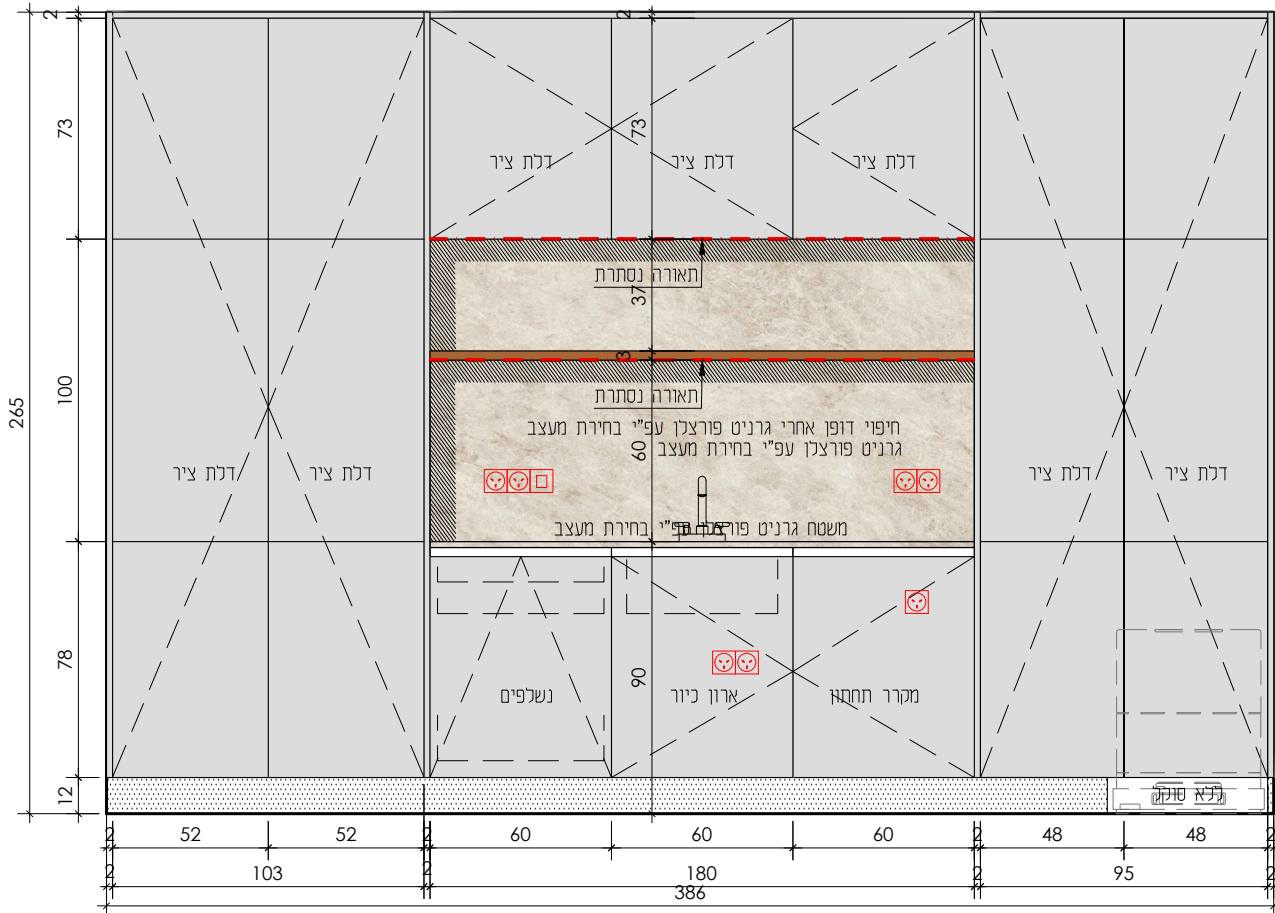

סידור פנימי
קנ"מ-1:20

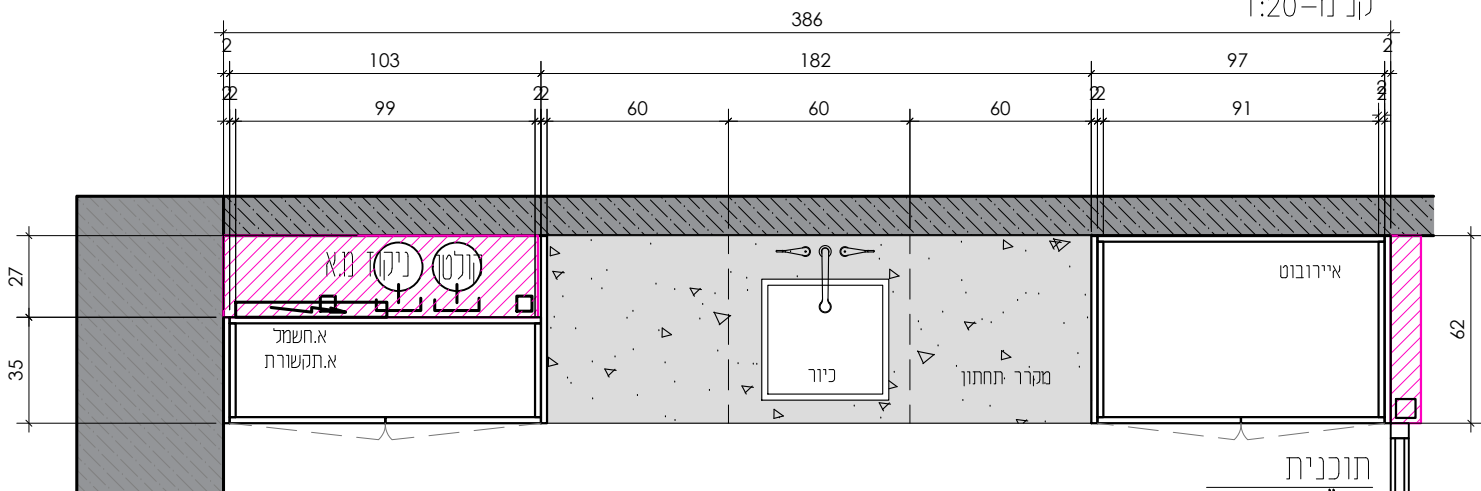


תוכנית
קנ"מ-1:20

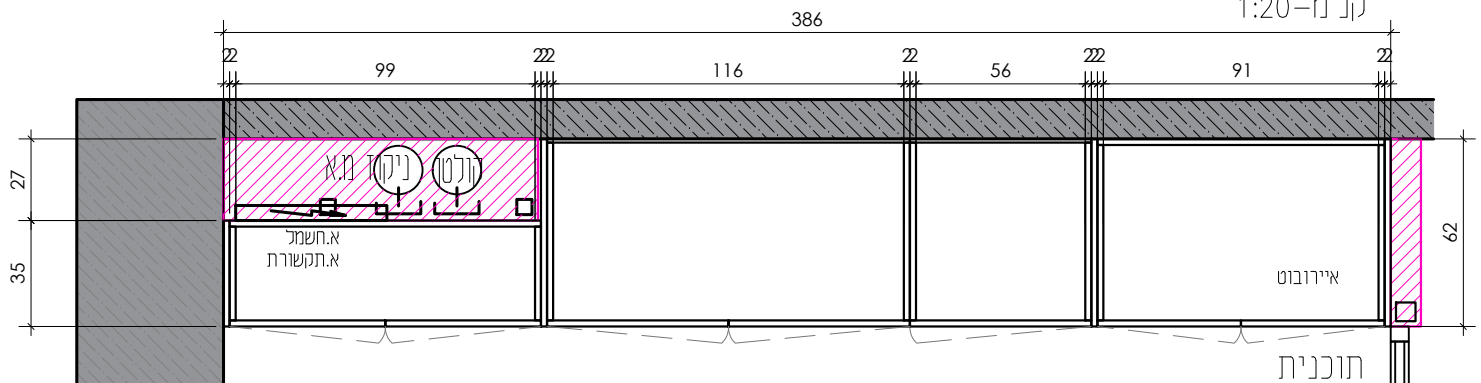


תוכנית
קנ"מ-1:20


1	שם		
12.12.25	תאריך:		
פורמיקה אפר בור עפ"י בחירת מתכנן עם קנט תואם לייזר פנים סנדוויץ גמר פורמיקה גוון אגוז מדיפים פנימים חלוקת חופשית +מעבד בוריה עפ"י הנחיות יועץ בטיחות	תאור		
ידית במה ופתיחה בסאף	פתיחה		
גרניט פורצילן - גוון עפ"י בחירת מעצב	משטח עריון		
גוון שחור	סוקל		
ידית במה ופתיחה בסאף מגירות "בכום" טריקה שקטה דלתות "בכום" טריקה שקטה מסילות וצירים	פרזול		
אביזרים נוספים			

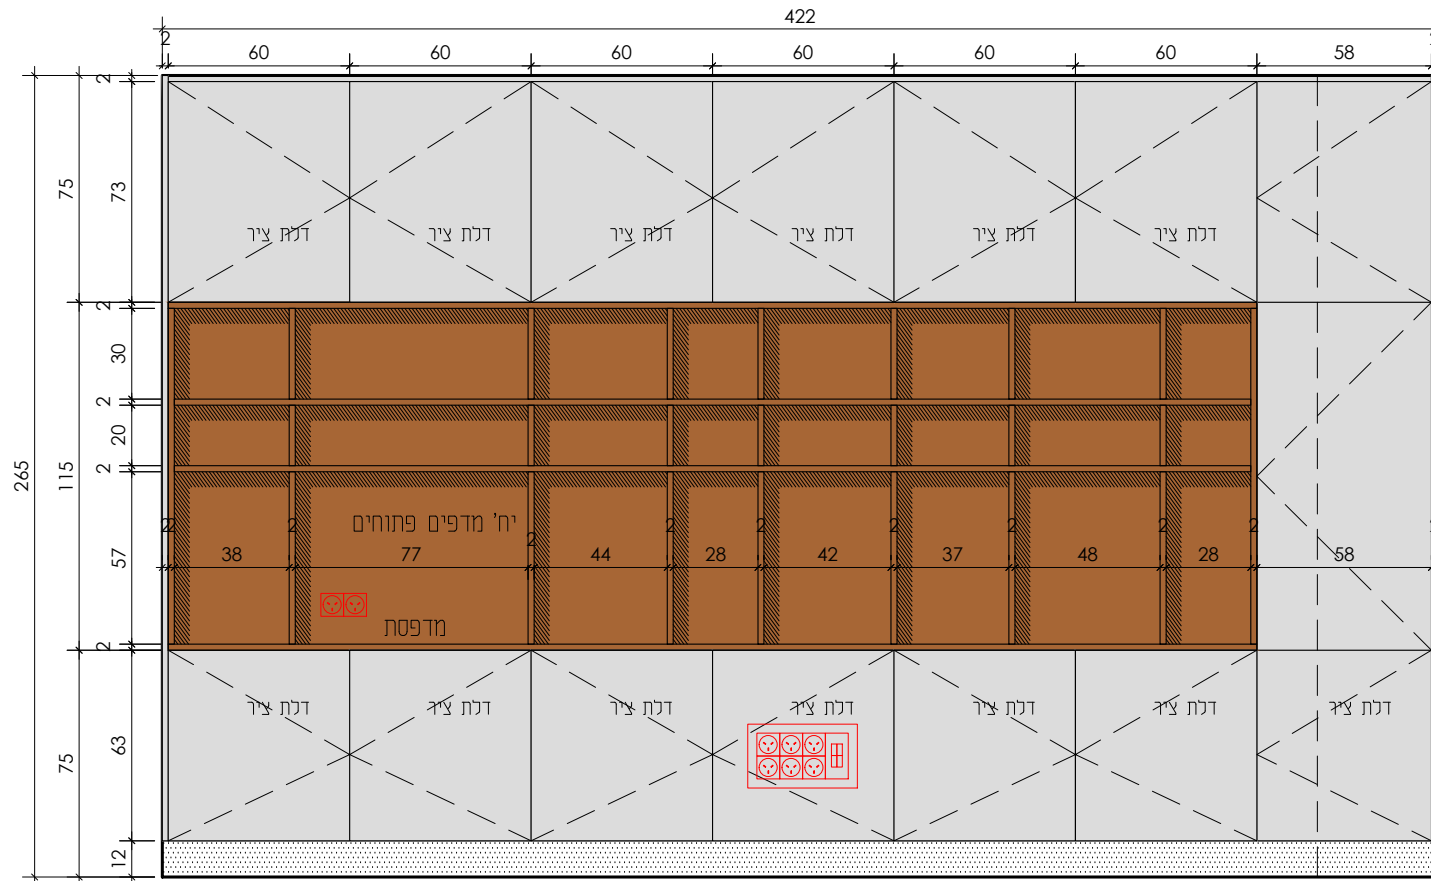

חזית
קנ"מ-1:20

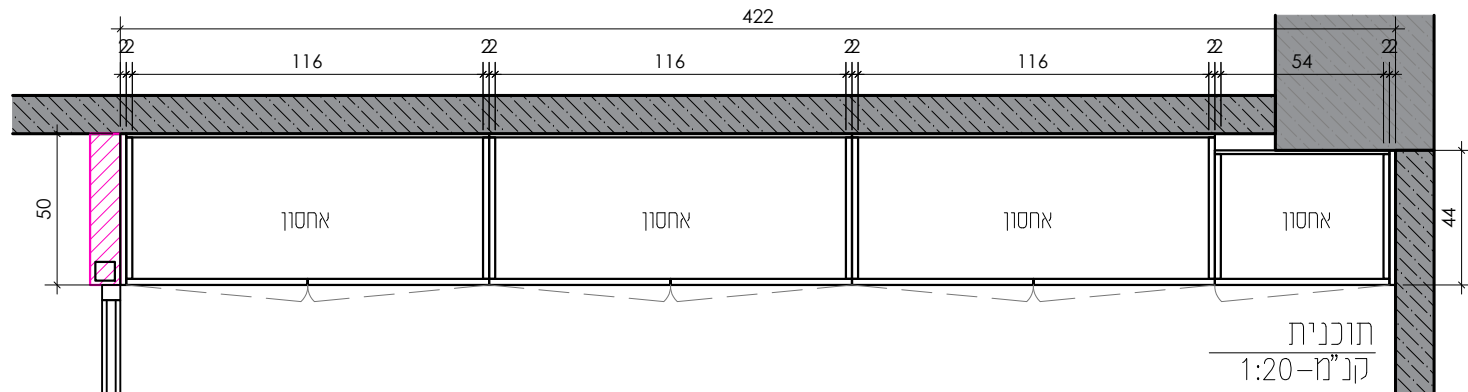

תוכנית
קנ"מ-1:20

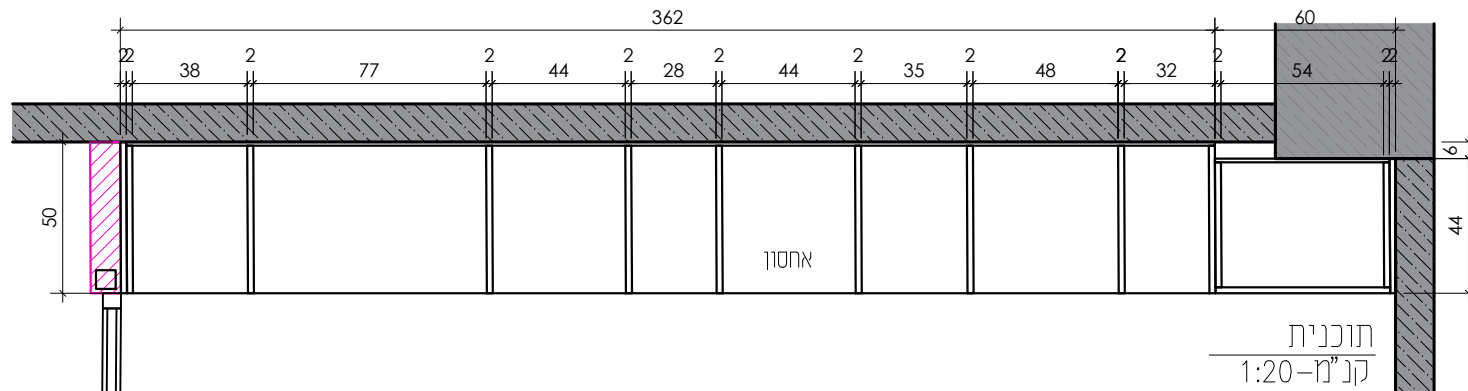

תוכנית
קנ"מ-1:20

נ 2	2	שם	
תאריך:	12.12.25		
תאור	פורמיקה אפור בהיר עפי' בחירת מתכנן עם קנט תואם לייזר פנים סנדוויץ' גמור פורמיקה גזון אגוז מדפים פנימים חזקת חופשית +מענב בהירה עפי' וחזיות יועץ בשיחות		
פתיחה	ידית במה ופתיחה בטאץ'		
משטח עליון	גרניט פורצינן - גוון עפי' בחירת מעצב		
סוקל	גוון שחור		
פרוזל	ידית	ידית במה ופתיחה בטאץ'	
	מגירות	"בלום" סריקה שקטה	
	דלתות	"בלום" סריקה שקטה	
	מסילות וצירים		
	אביזרים נוספים		